
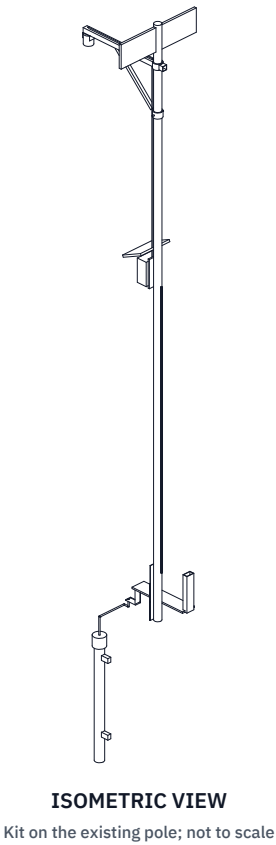


CONCEPT, NOT FOR FABRICATION
PRELIMINARY, NOT FOR FABRICATION

REV	DESCRIPTION	DATE	BY
P1	Preliminary GA for TRL 3 (from cad/src/model.py)	2026-09-25	AC
P2	DDR-002: lens 4.6 m, node 3.0 m, surface cable cover, anti-rotation bolt	2026-09-25	AC

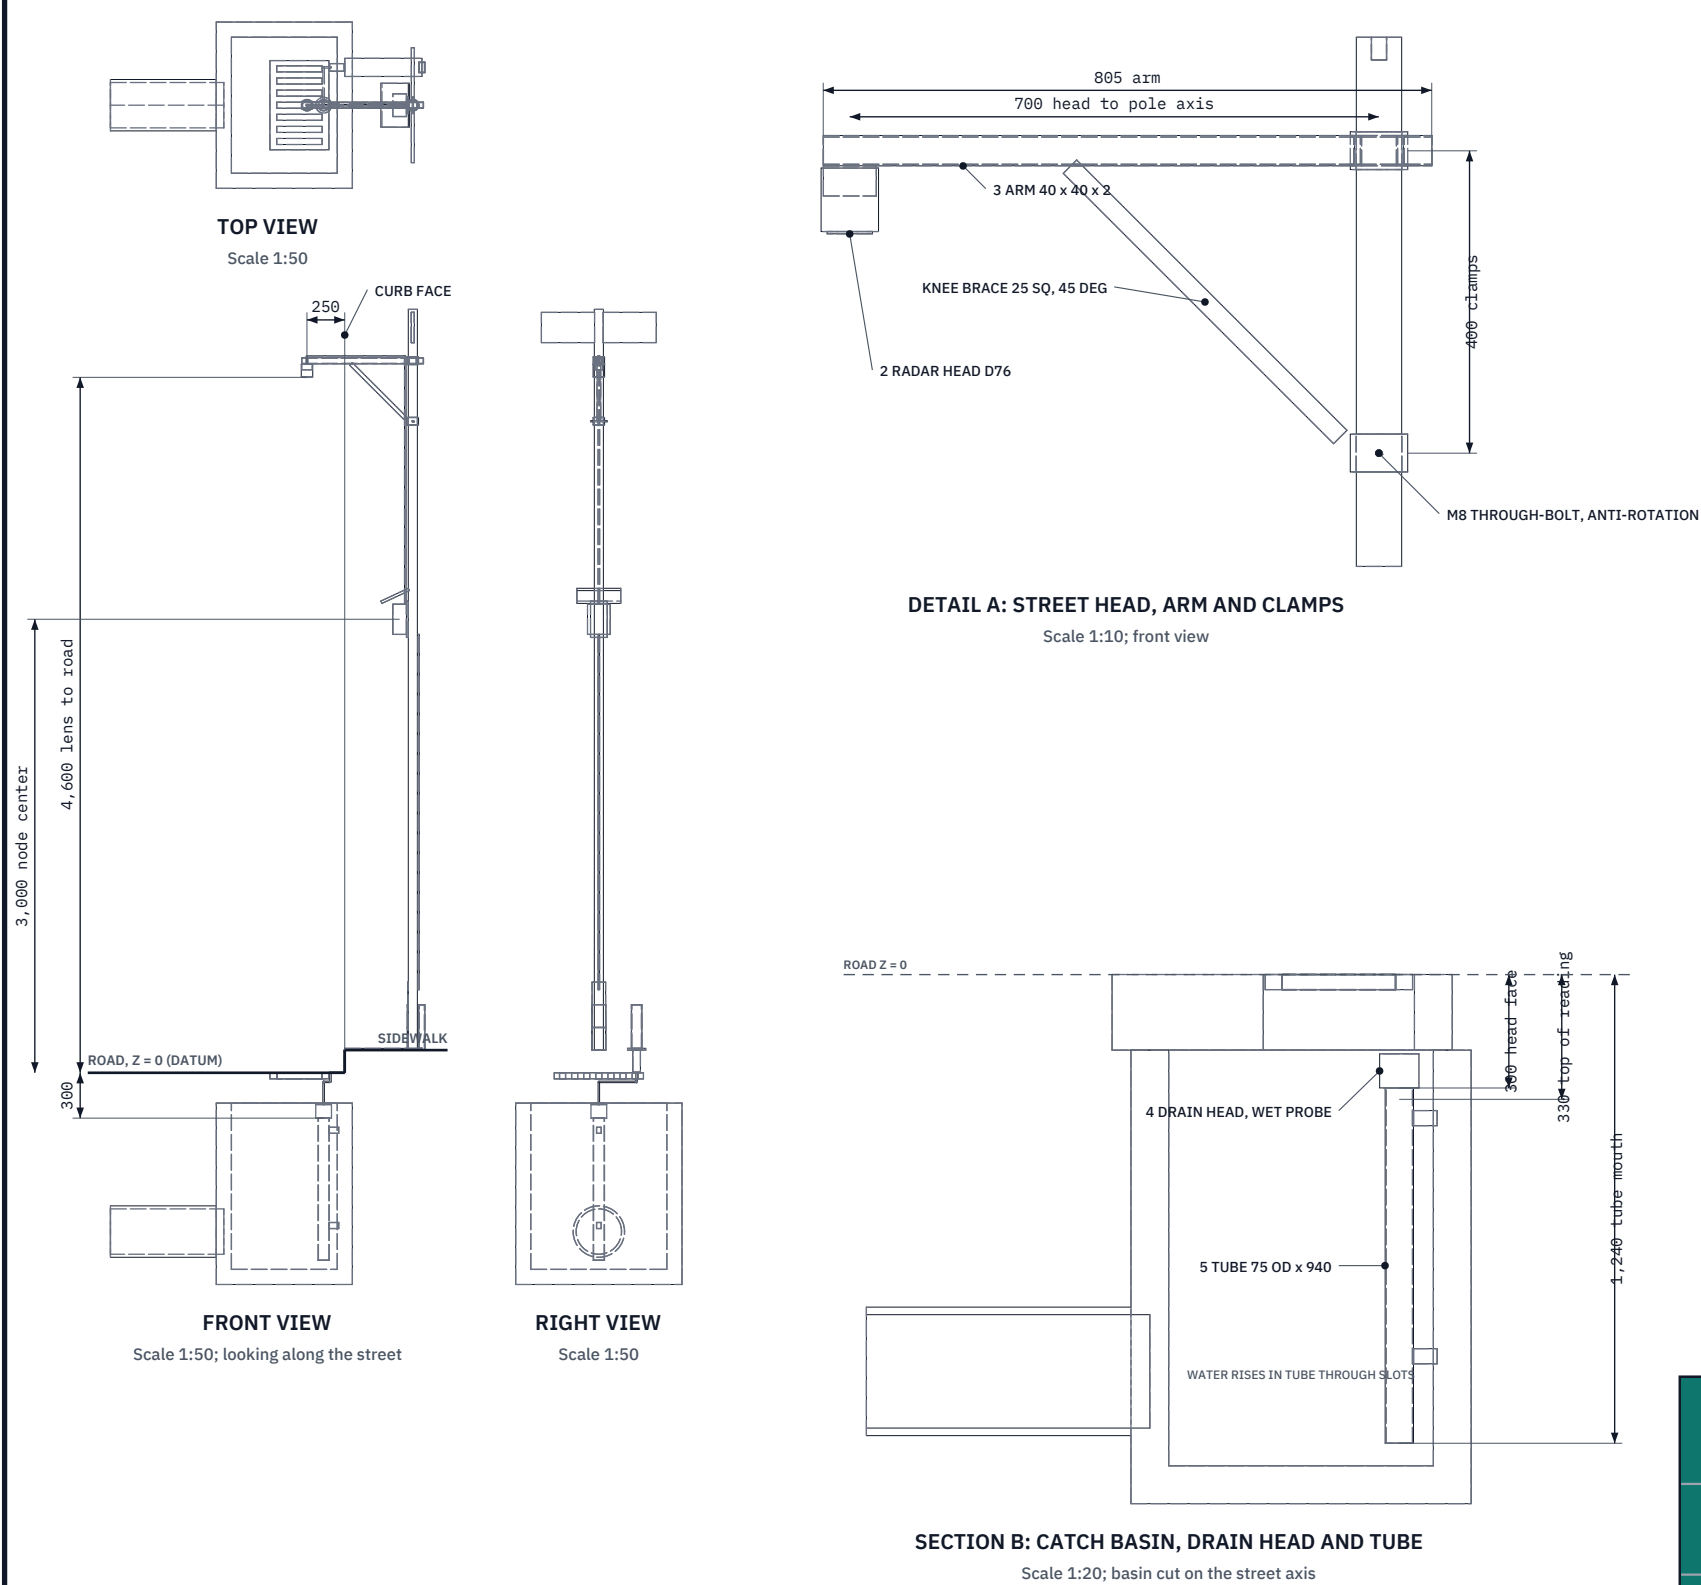

MAIN DIMENSIONS AND INTERFACES (MM)

Datum: road surface at the gauge point, Z = 0; curb 150

Radar lens 4,600 above road, 250 past curb face

Street depth 0 to 600: range 4,600 to 4,000

FieldNode 150 x 90 x 200 on 60 pole, center 3,000

Arm 40 sq x 805; band clamps 400 apart

Tube 75 OD, ID 69, 940 long, 40 slots 5 x 50

Drain reading 330 to 1,250 below road; probe 310

Pilot cable route: steel cover 760 long, curb and sidewalk anchors; riser guard

Marker bands 150 to 300 amber, 300 to 450 red

Lens height 2,500 to 5,000 per site, clearance rule (FLG-CAL-001 A7)

FLOODGAUGE					
General arrangement					
DRAWING NO. FLG-DWG-001			REV P2	SHEET 1 of 1	SIZE ANSI B
SCALE 1:50	UNITS mm	PROJECTION 	DATE 2026-09-25	DRAWN Amish Chadha	
MATERIAL / NOTES Aluminium arm, PVC tube, bought-in heads per bom/bom.csv; existing street shown for context. PRELIMINARY, NOT FOR FABRICATION					
Licensed CERN-OHL-S-2.0 · Design Molecule Lab · designmolecule.com				Generated from cad/src; do not edit by hand	