
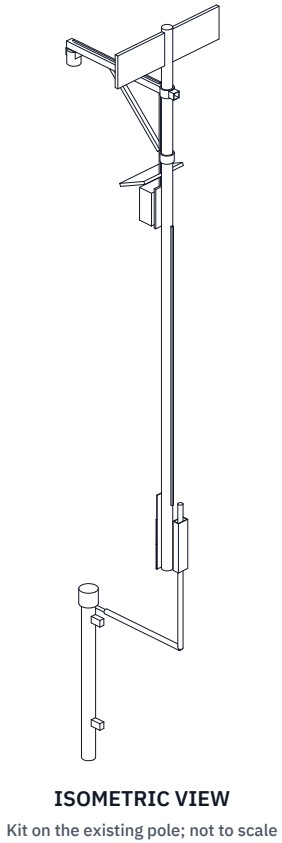
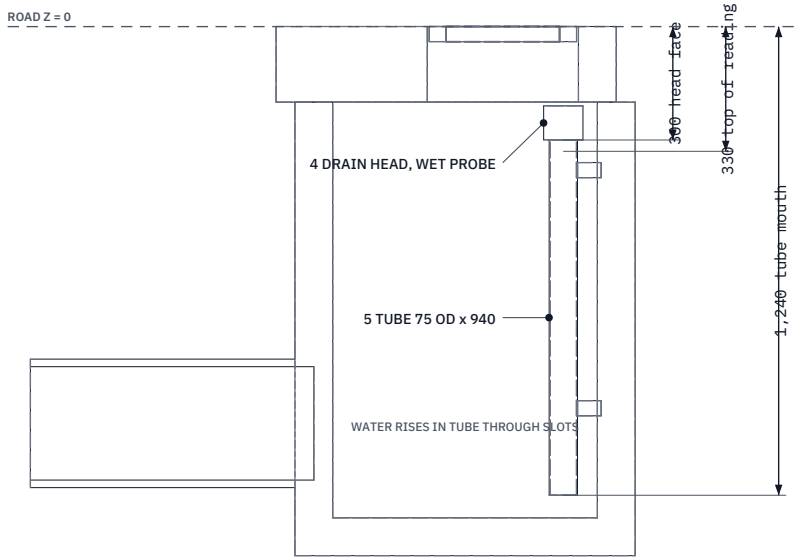
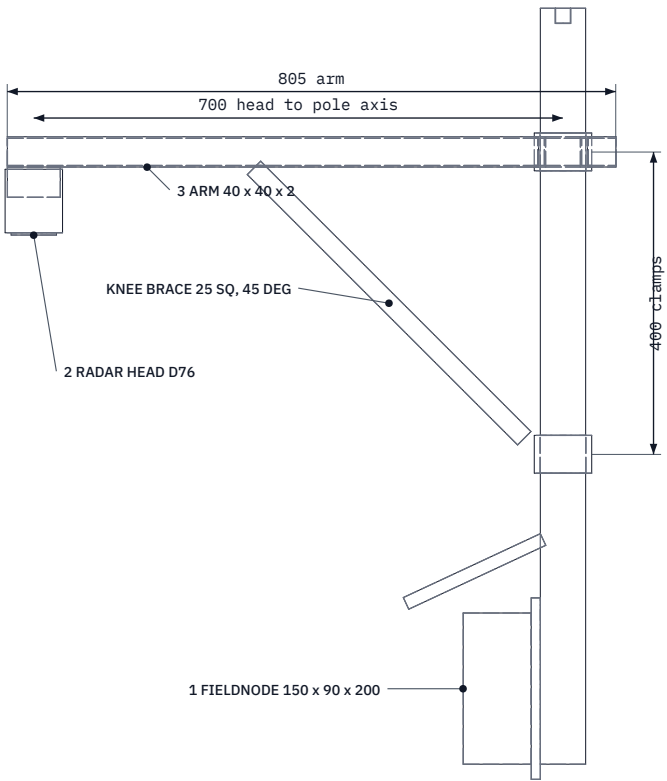


CONCEPT, NOT FOR FABRICATION
PRELIMINARY, NOT FOR FABRICATION

REV	DESCRIPTION	DATE	BY
P1	Preliminary GA for TRL 3 (from cad/src/model.py)	2026-09-25	AC

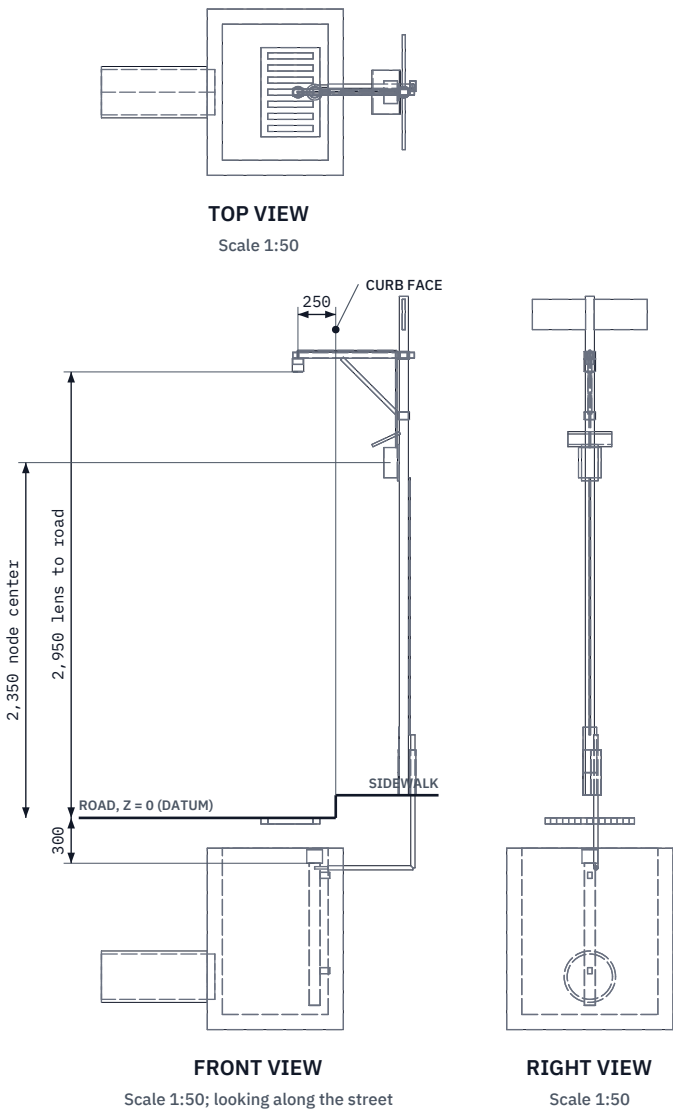

MAIN DIMENSIONS AND INTERFACES (MM)

Datum: road surface at the gauge point, Z = 0; curb 150
Radar lens 2,950 above road, 250 past curb face
Street depth 0 to 600: range 2,950 to 2,350
FieldNode 150 x 90 x 200 on 60 pole, center 2,350
Arm 40 sq x 805; band clamps 400 apart
Tube 75 OD, ID 69, 940 long, 40 slots 5 x 50
Drain reading 330 to 1,250 below road; probe 310
Conduit 25 at 330 below road; riser guard
Marker bands 150 to 300 amber, 300 to 450 red
Lens height to road authority rules (FLG-CAL-001 A7)

FLOODGAUGE

General arrangement

DRAWING NO. FLG-DWG-001		REV P1	SHEET 1 of 1	SIZE ANSI B
SCALE 1:50	UNITS mm	PROJECTION 	DATE 2026-09-25	DRAWN Amish Chadha
MATERIAL / NOTES Aluminium arm, PVC tube, bought-in heads per bom/bom.csv; existing street shown for context. PRELIMINARY, NOT FOR FABRICATION				
Licensed CERN-OHL-S-2.0 · Open Hardware Portfolio · amishchadha.com				Generated from cad/src; do not edit by hand