
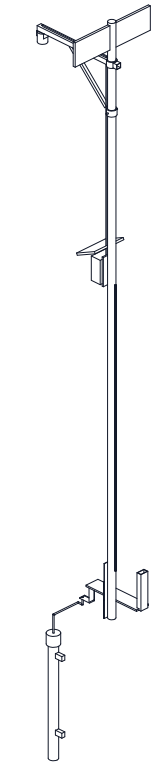


CONCEPT, NOT FOR FABRICATION
PRELIMINARY, NOT FOR FABRICATION

FloodGauge · github.com/BoujeeEnjinia1701/floodgauge

REV	DESCRIPTION	DATE	BY
P1	Preliminary GA for TRL 3 (from cad/src/model.py)	2026-09-25	AC
P2	DDR-002: lens 4.6 m, node 3.0 m, surface cable cover, anti-rotation bolt	2026-09-25	AC
P3	Layout and labels tidied	2026-09-25	AC

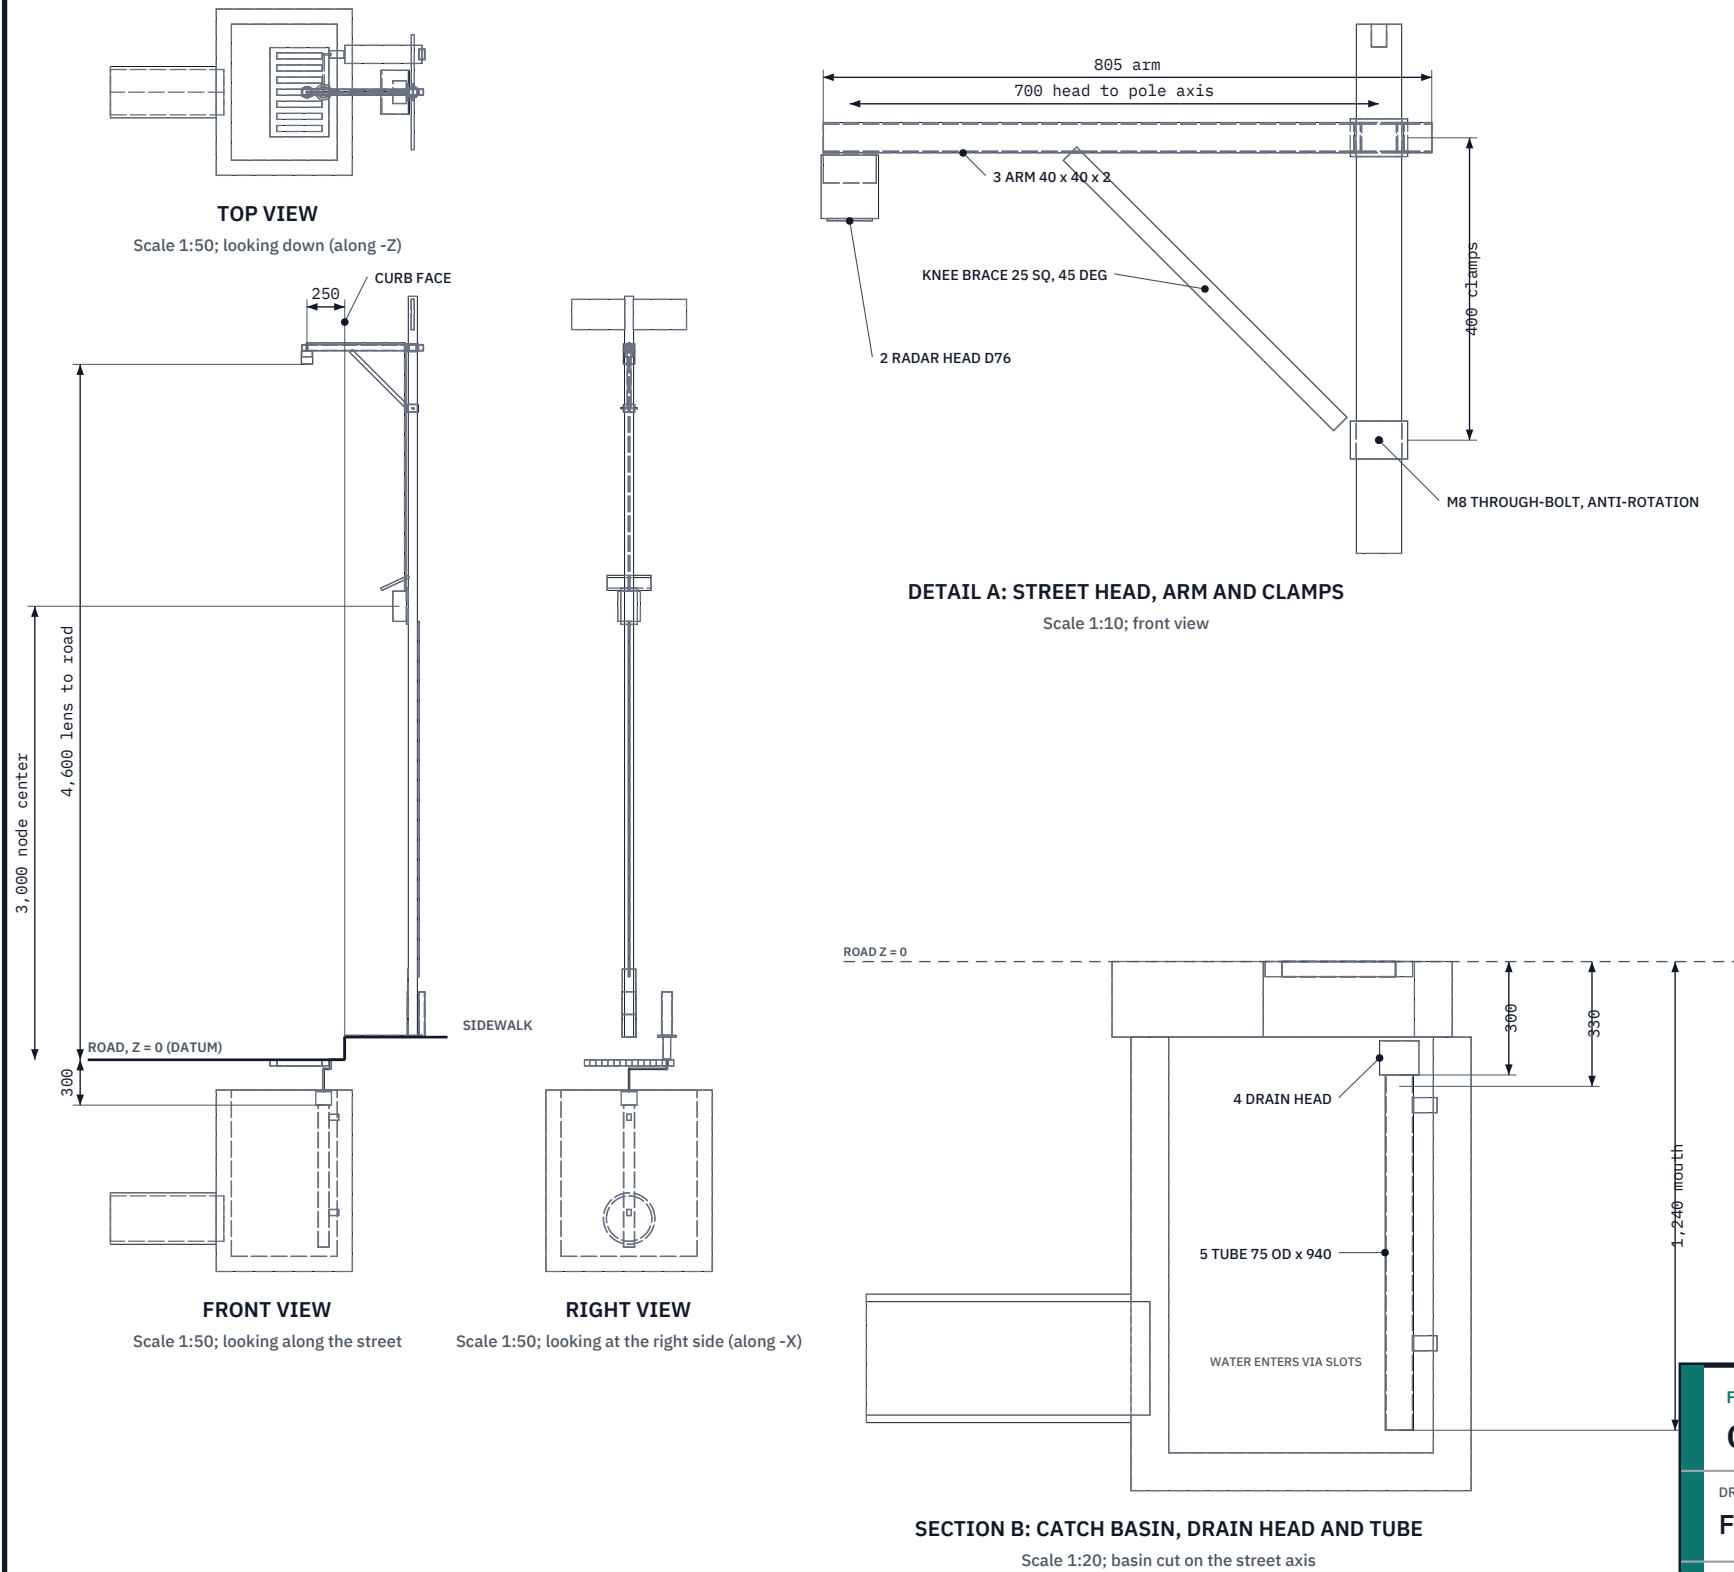

ISOMETRIC VIEW

Kit on the existing pole; not to scale; seen from the front right and above, about 30 deg elevation

MAIN DIMENSIONS AND INTERFACES (MM)

Datum: road surface at the gauge point, Z = 0; curb 150
Radar lens 4,600 above road, 250 past curb face
Street depth 0 to 600: range 4,600 to 4,000
FieldNode 150 x 90 x 200 on 60 pole, center 3,000
Arm 40 sq x 805; band clamps 400 apart
Tube 75 OD, ID 69, 940 long, 40 slots 5 x 50
Drain reading 330 to 1,250 below road; probe 310
Pilot cable route: steel cover 760 long, curb and sidewalk anchors; riser guard
Marker bands 150 to 300 amber, 300 to 450 red
Lens height 2,500 to 5,000 per site, clearance rule (FLG-CAL-001 A7)

FLOODGAUGE

github.com/BoujeeEnjinia1701/floodgauge

General arrangement

DRAWING NO. FLG-DWG-001		REV P3	SHEET 1 of 1	SIZE ANSI B
SCALE 1:50	UNITS mm	PROJECTION 	DATE 2026-09-25	DRAWN Amish Chadha
MATERIAL / NOTES Aluminium arm, PVC tube, bought-in heads per bom/bom.csv; existing street shown for context. PRELIMINARY, NOT FOR FABRICATION				
Licensed CERN-OHL-S-2.0 · Design Molecule Lab · designmolecule.com			Generated from cad/src; do not edit by hand	